

KETERANGAN :



: Lokasi Anda



 : Jalur Evakuasi

LAYOUT INSTALASI FIRE ALARM SYSTEM LANTAI BASEMENT
SKALA : 1 : 100






13 | 12 | 11 | 10 | 9 | 8 | 7 | 6 | 5 | 4 | 3 | 2



13 | 12 | 11 | 10 | 9 | 8 | 7 | 6 | 5 | 4 | 3 | 2

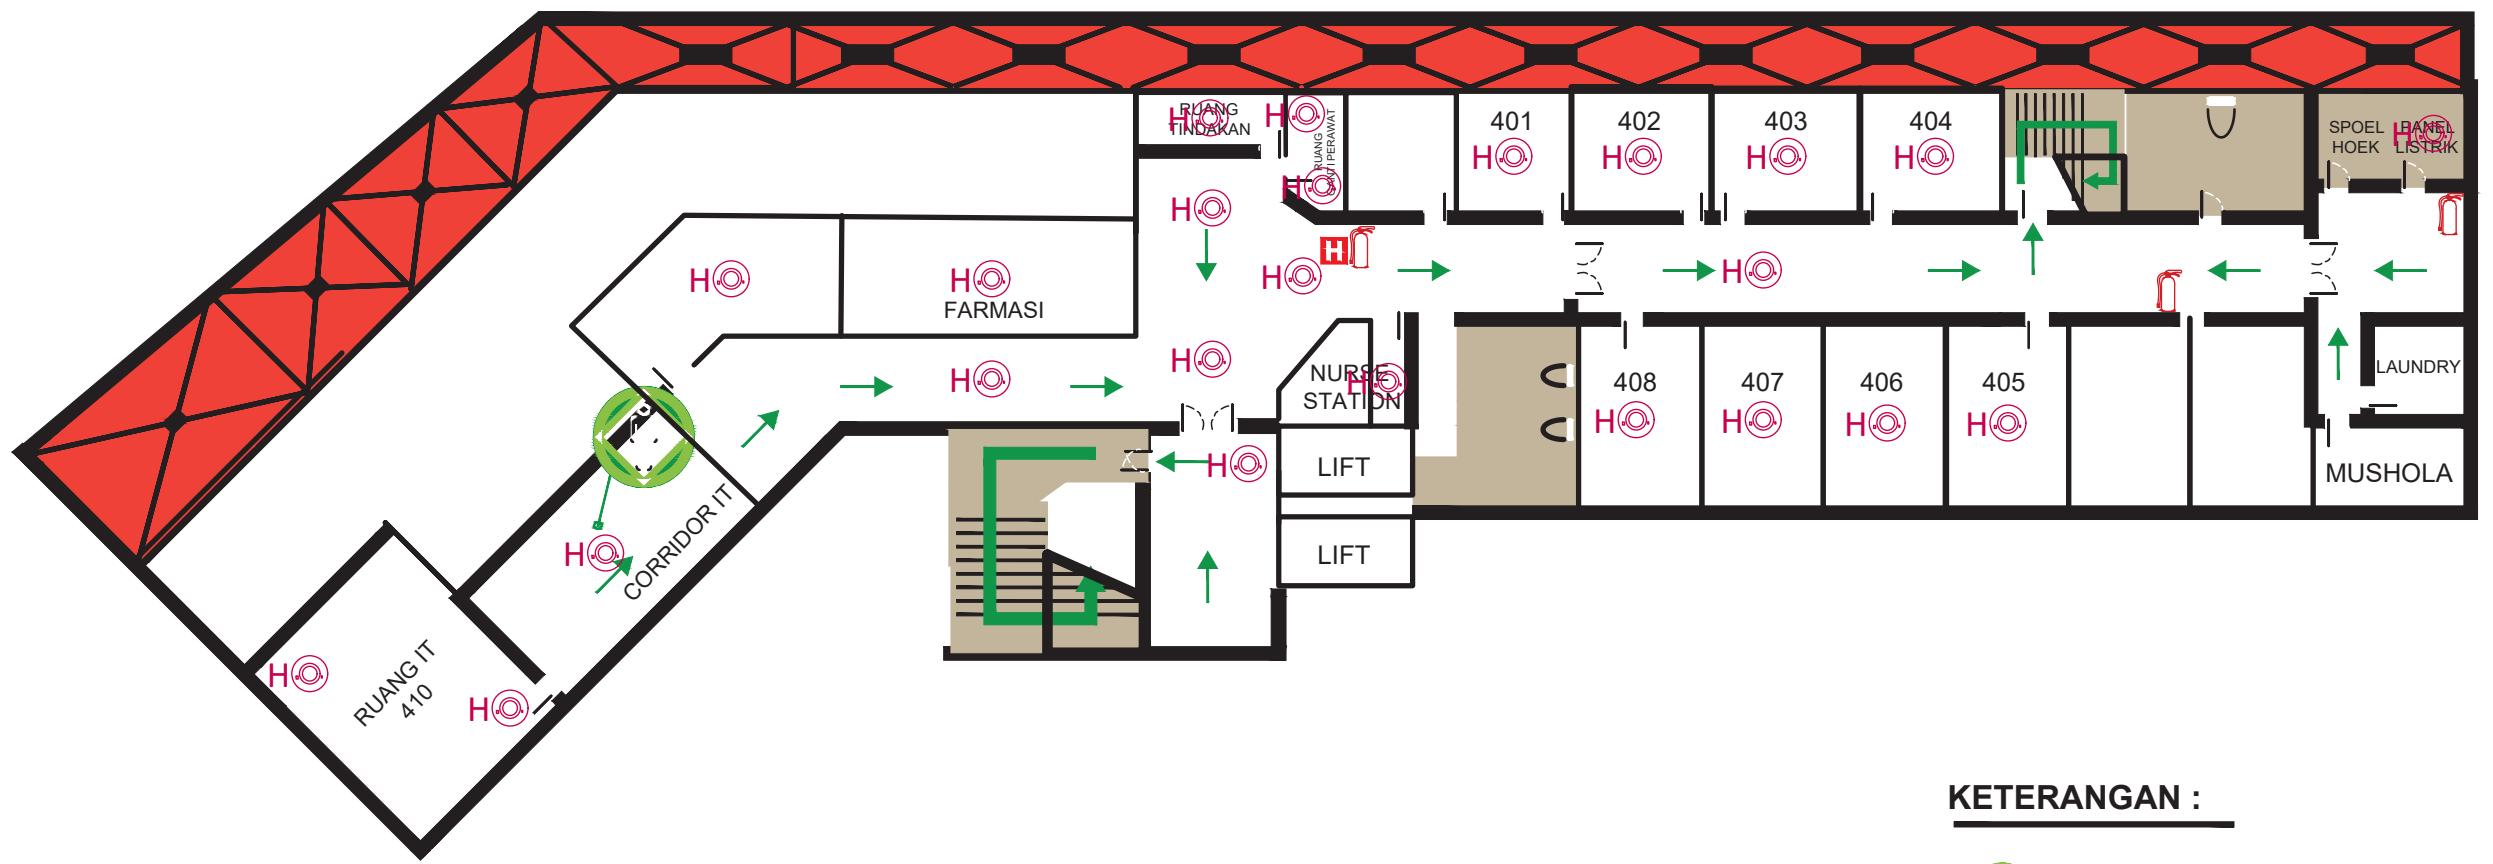

KETERANGAN :


- ◆ : Lokasi Anda
- : Jalur Evakuasi



LAYOUT INSTALASI FIRE ALARM SYSTEM LANTAI 4
SKALA : 1 : 100

14 | 13 | 12 | 11 | 10 | 9 | 8 | 7 | 6 | 5 | 4 | 3 | 2 | 1

| | | | |
|---|---|----------|------------------|
| PROYEK : | REVITALISASI FIRE ALARM SYSTEM GEDUNG RS ADHYAKSA | | |
| PEMBERI TUGAS : | RS ADHYAKSA | | |
| KONTRAKTOR : | CV. CANDRA PUTRA MADA CV. CANDRA PUTRA MADA CV. CANDRA PUTRA MADA CV. CANDRA PUTRA MADA | | |
| LEGEND : | <ul style="list-style-type: none">HO = 24 HEAT DETECTORAPAR = 3 APARH = 1 HYDRANT / ALARM | | |
| KEYPLAN : | | | |
| No | Revisi | Tgl | Paraf |
| PERSETUJUAN PEMBERI TUGAS : | | | |
| RS ADHYAKSA | | | |
| PENANGGUNG JAWAB : | | | |
| CV CANDRA PUTRA MADA | | | |
| NAMA GAMBAR : | | | |
| LAYOUT INSTALASI FIRE ALARM SYSTEM LANTAI 4 | | | |
| SKALA : | Digambar | Tgl | 04 NOVEMBER 2025 |
| 1 : 100 | Diperiksa | Tgl | |
| | Disetujui | Tgl | |
| Fase : | No. Gambar | | |
| SHOP DRAWING | | | 05 |
| Tanggal : | -- | Revisi : | -- |

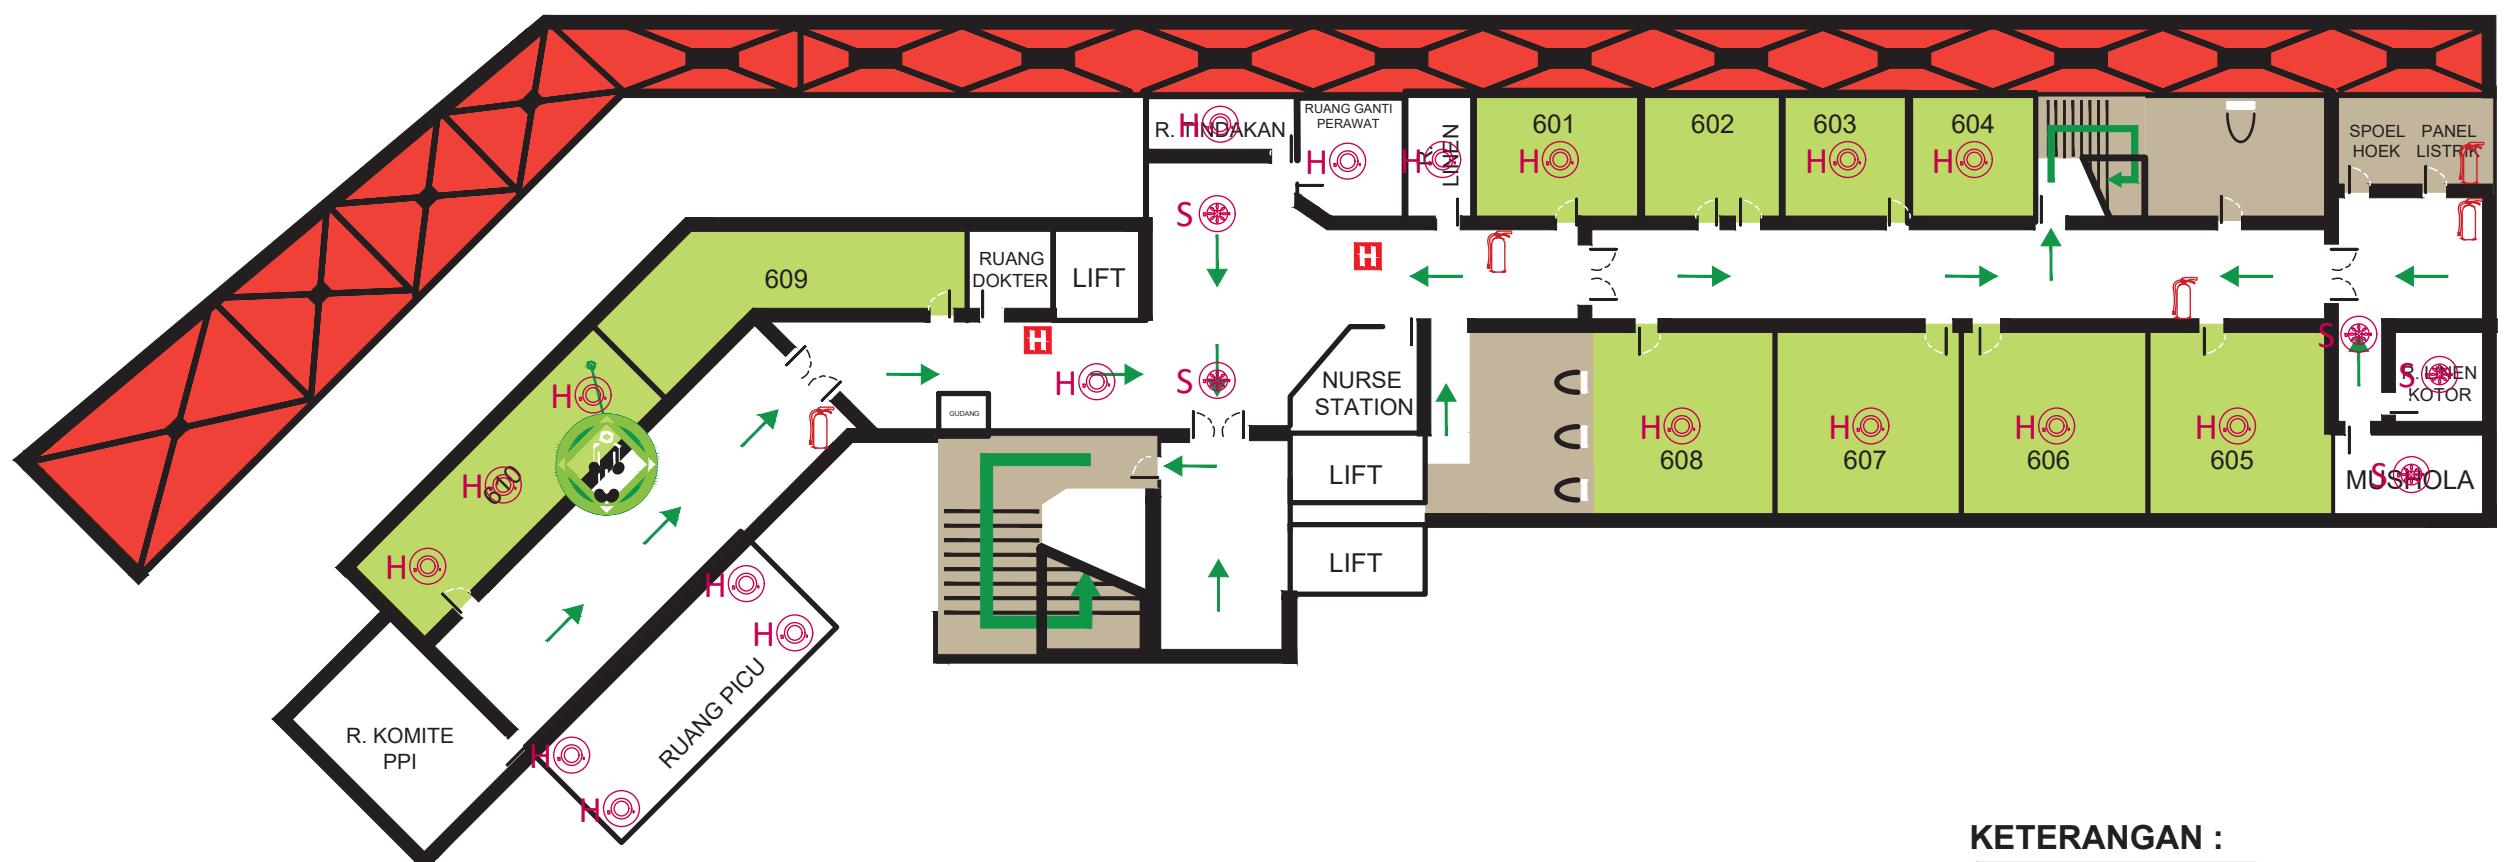

KETERANGAN :



: Lokasi Anda




 : Jalur Evakuasi

LAYOUT INSTALASI FIRE ALARM SYSTEM LANTAI 6
SKALA : 1 : 100

| | | | |
|---|---------------------|------------------------|-------|
| PROYEK : | | | |
| REVITALISASI FIRE ALARM SYSTEM GEDUNG RS ADHYAKSA | | | |
| PEMBERI TUGAS : | | | |
| RS ADHYAKSA | | | |
| KONTRAKTOR : | | | |
|  CV. CANDRA PUTRA MADA CONTRACTOR, SUPPLIER, PERGAWANGAN UMUM, JASA, ALAT TEKNIK MEKANIKAL, ELEKTRIKAL, MESIN-MESIN DAN PERLENGKAPANNYA, KOMPUTER, PRINTER, KAMERA, SISTEM PENGAMANAN, SISTEM PENGENDALIAN DAN MONITORING, dsb. Kuningan Barat, No. 10, RT. 001/RW. 001, Kelapa Gading, Kecamatan Kebayoran Baru, Jakarta Selatan 12110, Tel. 021-6754031, Hp. 081317845119, email: cvcandraputra@gmail.com | | | |
| CV CANDRA PUTRA MADA | | | |
| LEGEND : | | | |
|  | = 5 SMOKE DETECTOR | | |
|  | = 18 HEAT DETECTOR | | |
|  | = 5 APAR | | |
|  | = 2 HYDRANT / ALARM | | |
| KEYPLAN : | | | |
| No | Revisi | Tgl | Paraf |
| PERSETUJUAN PEMBERI TUGAS : | | | |
| RS ADHYAKSA | | | |
| PENANGGUNG JAWAB : | | | |
| CV CANDRA PUTRA MADA | | | |
| NAMA GAMBAR : | | | |
| LAYOUT INSTALASI FIRE ALARM SYSTEM LANTAI 6 | | | |
| SKALA : | Digambar | Tgl : 04 NOVEMBER 2025 | |
| 1 : 100 | Diperiksa | Tgl : | |
| | Disetujui | Tgl : | |
| Fase : | | No. Gambar | |
| SHOP DRAWING | | 07 | |
| Tanggal : | -- | Revisi : | -- |

13 | 12 | 11 | 10 | 9 | 8 | 7 | 6 | 5 | 4 | 3 | 2

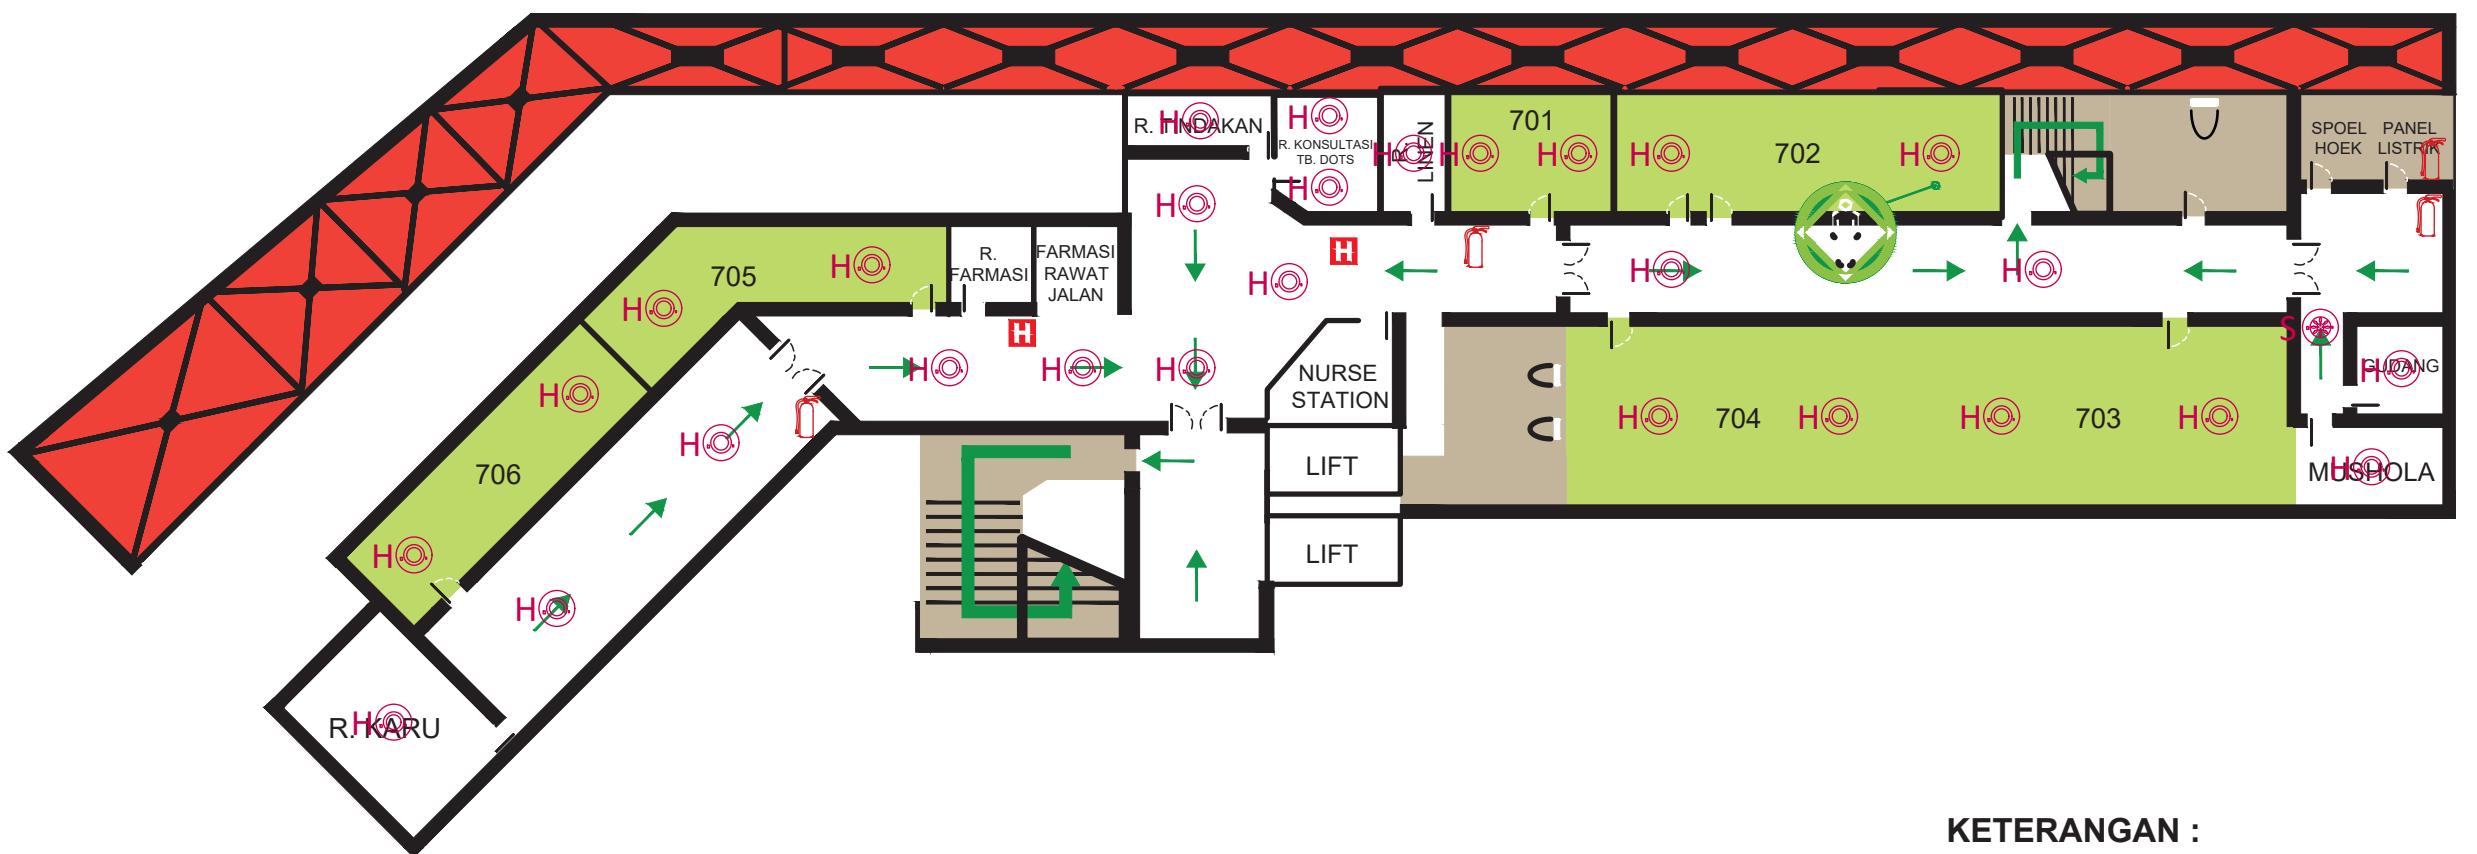

KETERANGAN :



: Lokasi Anda




: Jalur Evakuasi



LAYOUT INSTALASI FIRE ALARM SYSTEM LANTAI 7
SKALA : 1 : 100

| |
|---|
| PROYEK : | REVITALISASI FIRE ALARM SYSTEM GEDUNG RS ADHYAKSA | |
| PEMBERI TUGAS : | RS ADHYAKSA | |
| KONTRAKTOR : | CV. CANDRA PUTRA MADA CV. CANDRA PUTRA MADA CV. CANDRA PUTRA MADA CV. CANDRA PUTRA MADA | |
| LEGEND : | <ul style="list-style-type: none">= 1 SMOKE DETECTOR= 28 HEAT DETECTOR= 4 APAR= 2 HYDRANT / ALARM | |
| KEYPLAN : | <table border="1"><tr><td>No</td><td>Revisi</td><td>Tgl</td><td>Paraf</td></tr><tr><td colspan="4">PERSETUJUAN PEMBERI TUGAS :</td></tr><tr><td colspan="4">RS ADHYAKSA</td></tr><tr><td colspan="4">PENANGGUNG JAWAB :</td></tr><tr><td colspan="4">CV CANDRA PUTRA MADA</td></tr><tr><td colspan="4">NAMA GAMBAR :</td></tr><tr><td colspan="4">LAYOUT INSTALASI FIRE ALARM SYSTEM LANTAI 7</td></tr><tr><td>SKALA :</td><td>Digambar</td><td>Tgl</td><td>04 NOVEMBER 2025</td></tr><tr><td>1 : 100</td><td>Diperiksa</td><td>Tgl</td><td></td></tr><tr><td></td><td>Disetujui</td><td>Tgl</td><td></td></tr><tr><td>Fase :</td><td colspan="3">No. Gambar</td></tr><tr><td colspan="3">SHOP DRAWING</td><td>08</td></tr><tr><td>Tanggal :</td><td>--</td><td>Revisi :</td><td>--</td></tr></table> | | | No | Revisi | Tgl | Paraf | PERSETUJUAN PEMBERI TUGAS : | | | | RS ADHYAKSA | | | | PENANGGUNG JAWAB : | | | | CV CANDRA PUTRA MADA | | | | NAMA GAMBAR : | | | | LAYOUT INSTALASI FIRE ALARM SYSTEM LANTAI 7 | | | | SKALA : | Digambar | Tgl | 04 NOVEMBER 2025 | 1 : 100 | Diperiksa | Tgl | | | Disetujui | Tgl | | Fase : | No. Gambar | | | SHOP DRAWING | | | 08 | Tanggal : | -- | Revisi : | -- |
| No | Revisi | Tgl | Paraf | |
| PERSETUJUAN PEMBERI TUGAS : | |
| RS ADHYAKSA | |
| PENANGGUNG JAWAB : | |
| CV CANDRA PUTRA MADA | |
| NAMA GAMBAR : | |
| LAYOUT INSTALASI FIRE ALARM SYSTEM LANTAI 7 | |
| SKALA : | Digambar | Tgl | 04 NOVEMBER 2025 | |
| 1 : 100 | Diperiksa | Tgl | |
| | Disetujui | Tgl | |
| Fase : | No. Gambar | |
| SHOP DRAWING | | | 08 | |
| Tanggal : | -- | Revisi : | -- | |

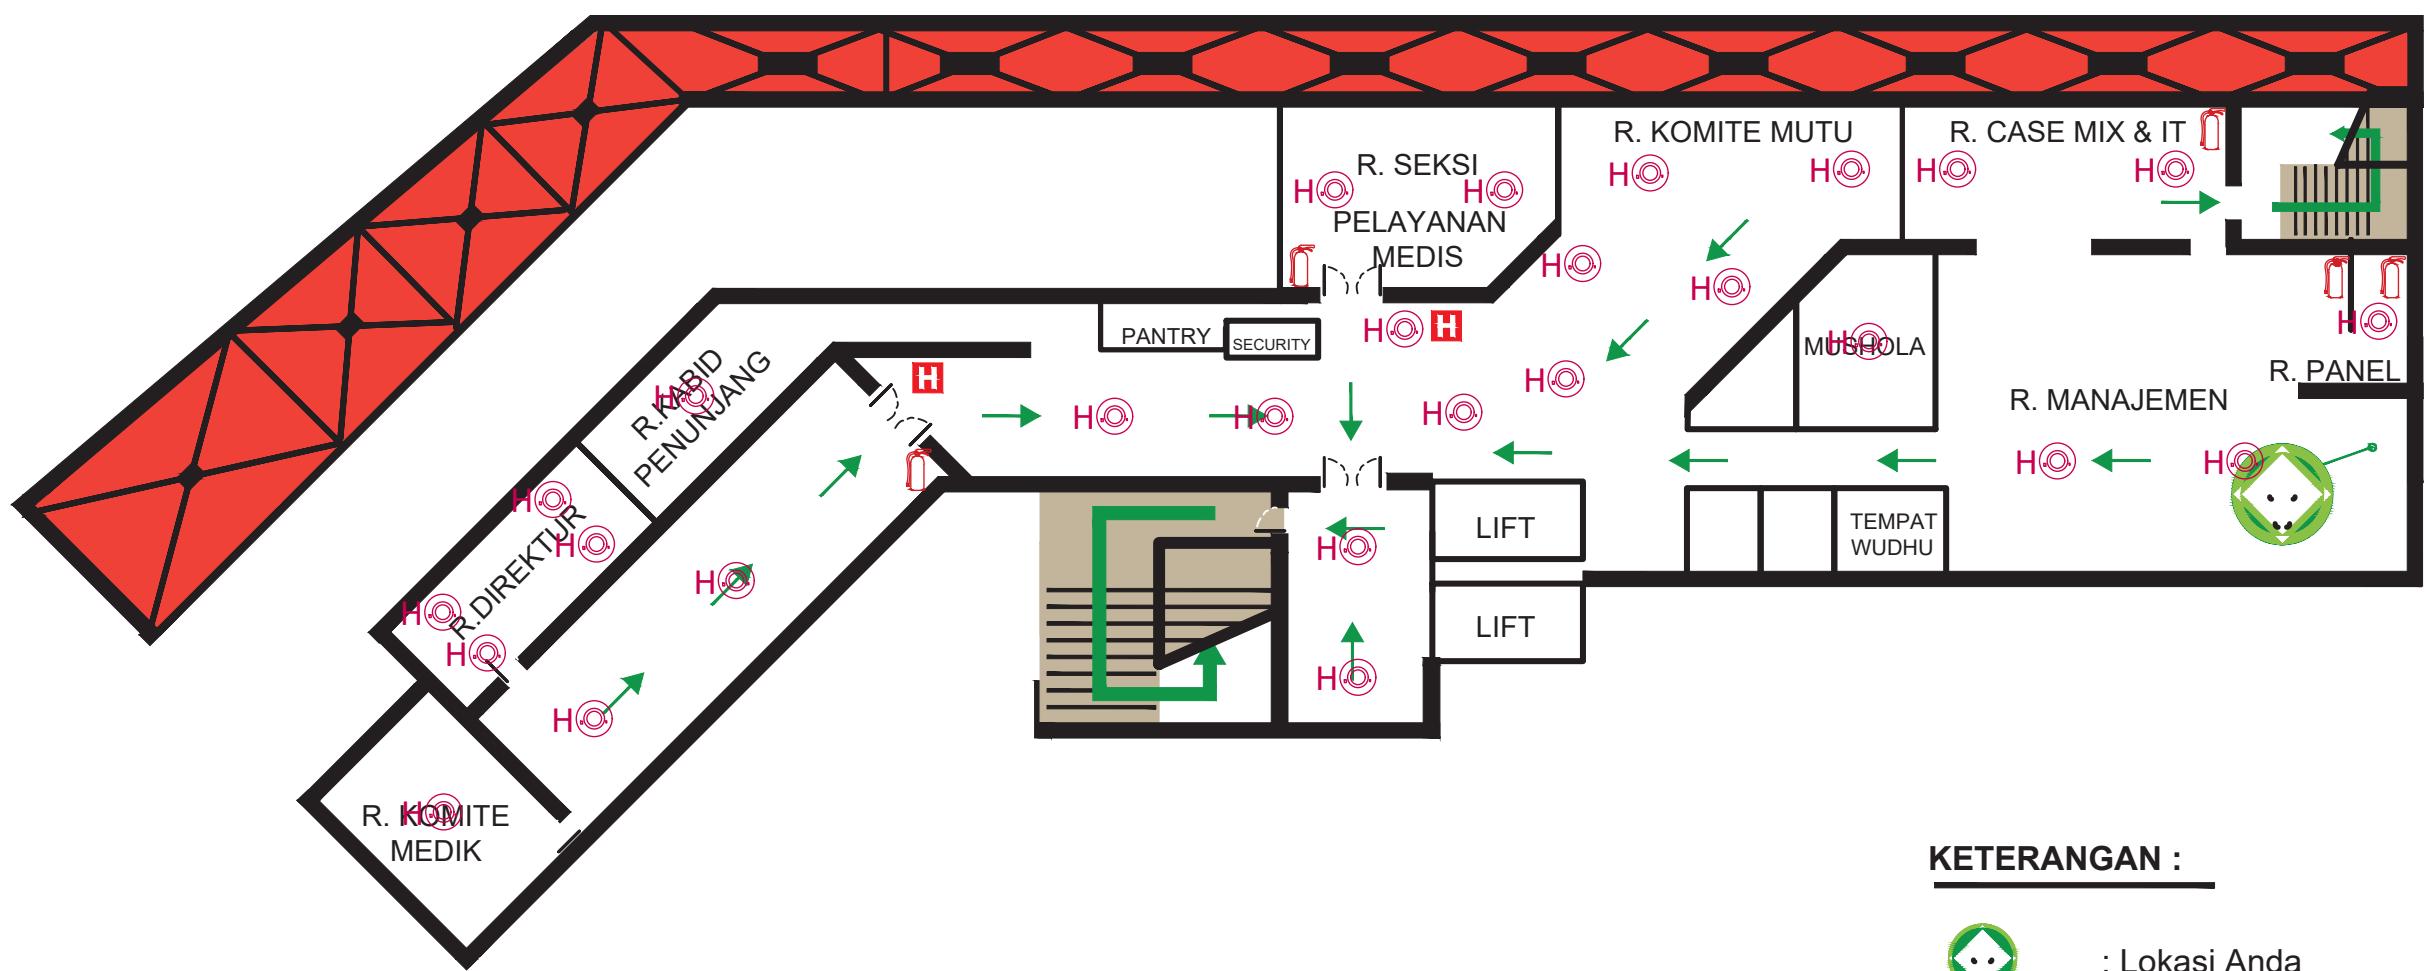

KETERANGAN :



: Lokasi Anda



 : Jalur Evakuasi

LAYOUT INSTALASI FIRE ALARM SYSTEM LANTAI 8
SKALA : 1 : 100

| | | | |
|--|---------------------|------------|------------------|
| PROYEK : | | | |
| REVITALISASI FIRE ALARM SYSTEM GEDUNG RS ADHYAKSA | | | |
| PEMBERI TUGAS : | | | |
| RS ADHYAKSA | | | |
| KONTRAKTOR : | | | |
|  CV. CANDRA PUTRA MADA CONTRACTOR, SUPPLIER, PERAGANGAN DINI, JASA, ALAT TENIK MEKANIK ELEKTRIKAL, MESIN-MESIN DAN BERPENGARUH PADA KEGIATAN INDUSTRI Kompleks Perindustrian dan Perdagangan PIK 181 R/027/Bw-Dk Kel. Kelapa Dua Wilayah, Kec. Cicendo Jakarta Timur, Tlp. 021-6704001, Hp. 081317345178, email: cvcandraputra@gmail.com | | | |
| CV CANDRA PUTRA MADA | | | |
| LEGEND : | | | |
|  | = 27 HEAT DETECTOR | | |
|  | = 5 APAR | | |
|  | = 2 HYDRANT / ALARM | | |
| KEYPLAN : | | | |
| No | Revisi | Tgl | Paraf |
| PERSETUJUAN PEMBERI TUGAS : | | | |
| RS ADHYAKSA | | | |
| PENANGGUNG JAWAB : | | | |
| CV CANDRA PUTRA MADA | | | |
| NAMA GAMBAR : | | | |
| LAYOUT INSTALASI FIRE ALARM SYSTEM LANTAI 8 | | | |
| SKALA : | Digambar | Tgl | 04 NOVEMBER 2025 |
| 1 : 100 | Diperiksa | Tgl | |
| | Disetujui | Tgl | |
| Fase : | | No. Gambar | |
| SHOP DRAWING | | 09 | |
| Tanggal : | -- | Revisi : | -- |